
Принципиальная гидравлическая схема водоотлива

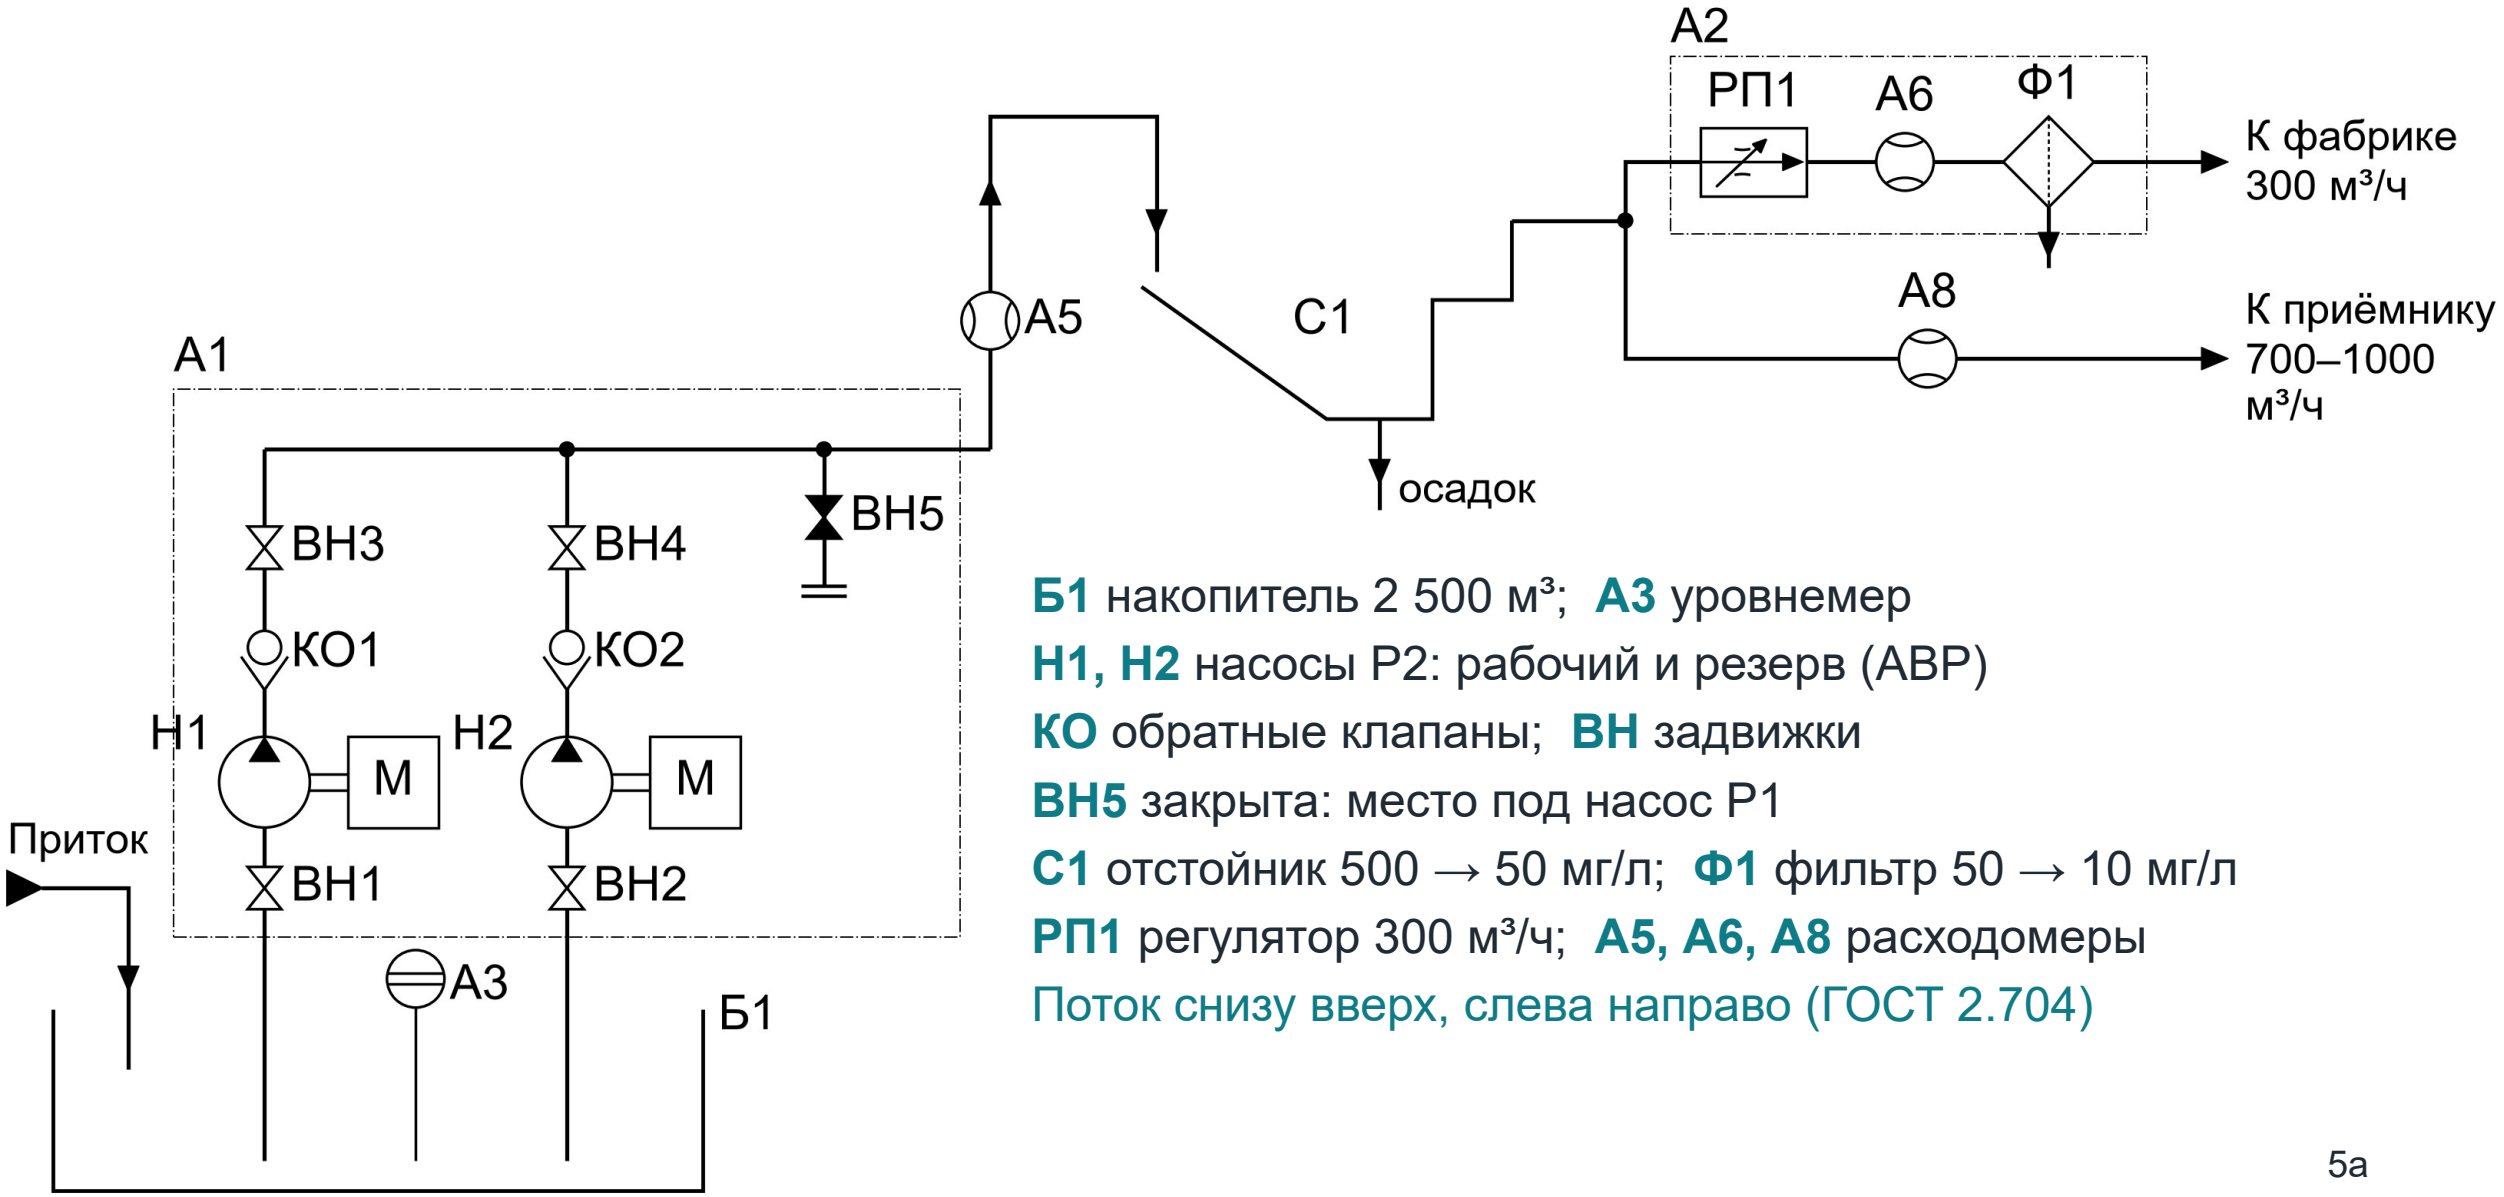

Б1 накопитель 2 500 м³; **А3** уровнемер

Н1, Н2 насосы Р2: рабочий и резерв (АВР)

КО обратные клапаны; **ВН** задвижки

ВН5 закрыта: место под насос Р1

С1 отстойник 500 → 50 мг/л; **Ф1** фильтр 50 → 10 мг/л

РП1 регулятор 300 м³/ч; **А5, А6, А8** расходомеры

Поток снизу вверх, слева направо (ГОСТ 2.704)